NOTES

1. REFER TO DRAWING SP/SD-001.00 FOR FIRE PROTECTION LEGENDS, ABBREVIATIONS, NOTES, AND SCHEDULES.

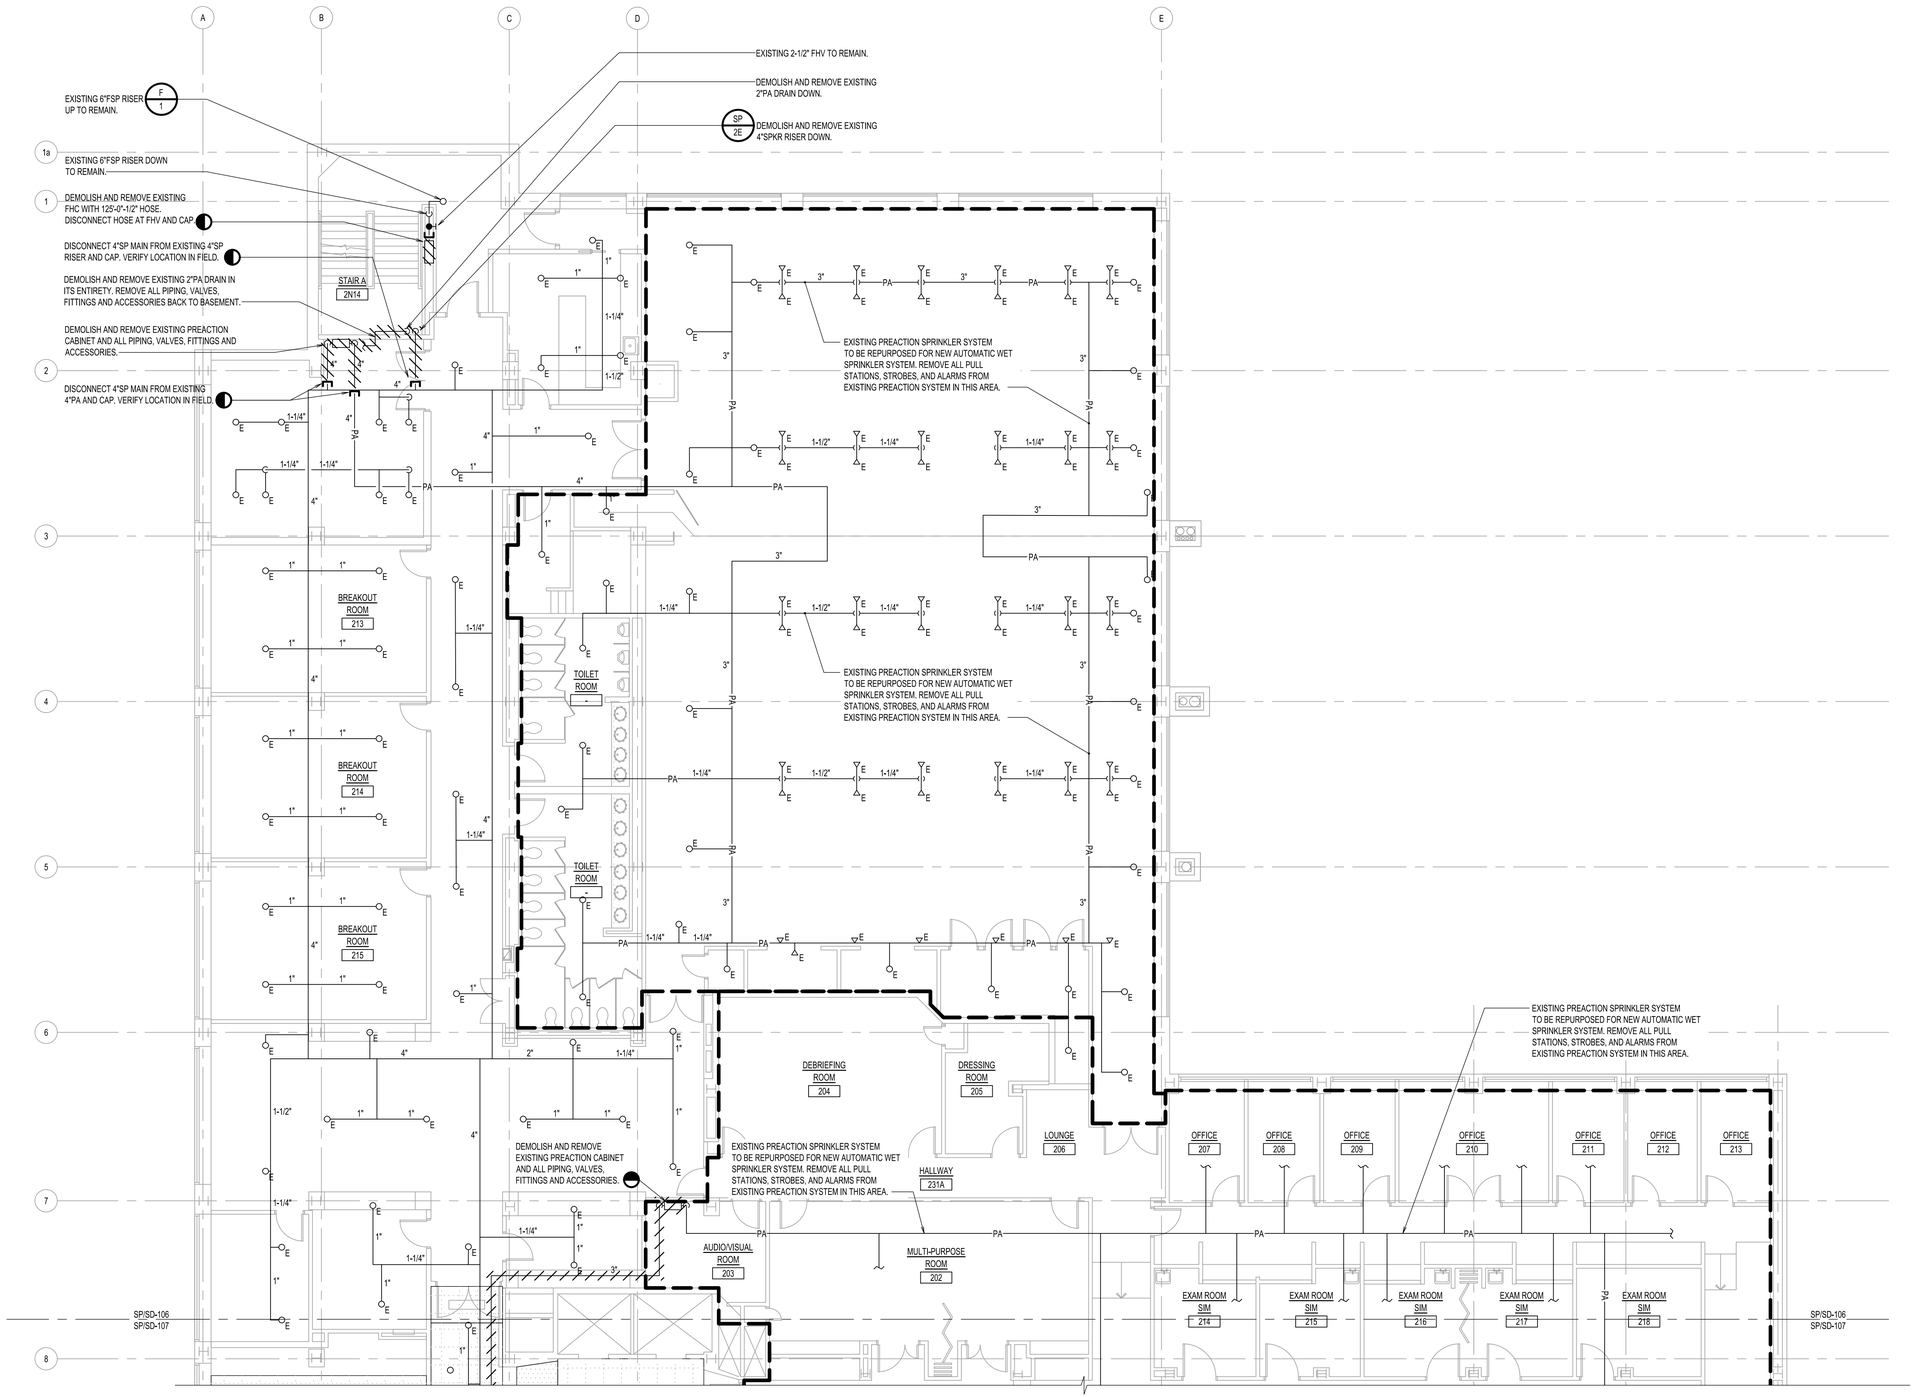

N

SECOND FLOOR NORTH FIRE PROTECTION DEMOLITION PLAN

SCALE: 1/8"=1'0"

NEW YORK CITY BUILDING DEPARTMENT NOTE:

"THIS PLAN IS SUBMITTED FOR APPROVAL BY THE NEW YORK CITY BUILDING DEPARTMENT ONLY FOR WORK INDICATED ON THE APPLICATION SPECIFICATION SHEET. ALL OTHER MATTERS SHOWN ARE NOT TO BE RELIED UPON, OR TO BE CONSIDERED AS, EITHER BEING APPROVED OR IN ACCORDANCE WITH APPLICABLE CODES."

MEP ENGINEER:

LIZARDOS

LONG ISLAND | NEW YORK CITY | CHARLOTTE | DANBURY

200 Old Country Road | Suite 670
Mineola | NY 11501
516 484 1020 Lizardos.com

Lizardos Engineering and Architecture Consultants P.C.

Architect:

RICHARD GONZALEZ ARCHITECT, PLLC
2 Beechtree Lane
Bronxville, NY 10708
646.763.2409
rg@rgitect.com

Environmental:

Watts Architects &Engineers

NO.	REVISION	DATE
5	ISSUED FOR BID	04-14-23
4	ISSUED FOR OWNER REVIEW	11-23-22
3	ISSUED FOR BID	11-11-22
2	90% BID/FILING REVIEW	06-24-22
1	ISSUED FOR 60% PROGRESS REVIEW	04-15-22

IT IS A VIOLATION OF THE NEW YORK STATE EDUCATION LAW FOR ANY PERSON, UNLESS ACTING UNDER THE DIRECTION OF A LICENSED PROFESSIONAL ENGINEER, TO ALTER ANY ITEM ON THIS DRAWING AND/OR RELATED SPECIFICATION. ALL ALTERATIONS MUST BE MADE IN COMPLIANCE WITH THE NEW YORK STATE EDUCATION LAW. THE PROFESSIONAL ENGINEER WHOSE SEAL APPEARS HEREON ASSUMES NO RESPONSIBILITY FOR ANY SUCH ALTERATION OR RE-USE WITHOUT HIS WRITTEN CONSENT.

SEAL:

CLIENT:

NYC HEALTH+ HOSPITALS

JACOBI MEDICAL CENTER
1400 PELHAM PKWY SOUTH,
BRONX, NY 10461

PROJECT TITLE:

NYC HHC JACOBI MEDICAL CENTER, BRONX, NY BUILDING 4 SPRINKLER AND FIRE ALARM UPGRADE

DRAWING TITLE:

FIRE PROTECTION SECOND FLOOR PLAN NORTH - DEMOLITION

DRAWN BY:	JJA	SCALE:	AS NOTED
DESIGNED BY:	JJA	DATE:	04-15-22
CHECKED BY:	RS	PROJECT NO:	10472
CADD FILENAME:	10472-FP-106.dwg		
PLOTTED BY:	DVSWeissman	PLOT DATE:	5/04/23 6:09 PM

DRAWING NO:

SP/SD-106.00

DOB SIGNATURE / STAMP

DOB BISCAN

SHEET: 8 OF 39